BAUHERRSCHAFT MARTHA UND DANIEL GANTENBEIN PLATZ 7306 FLÄSCH

ERWEITERUNG WEINGUT GANTENBEIN, 7306 FLÄSCH

PLAN NR.	6a_osw
MASSTAB	1:50
FORMAT	A0
DATUM	27.01.2006
INDEX	G

AUSFÜHRUNGSPLAN
FASSADEN OST / SÜD / WEST

BEARTH & DEPLAZES ARCHITEKTEN AG
VALENTIN BEARTH ANDREA DEPLAZES DANIEL LADNER
WIESENTALSTRASSE 7 7000 CHUR TEL. 081 354 93 00 FAX. 081 354 93 01
HARDTURMSTRASSE 123 8005 ZÜRICH TEL. 044 355 51 41 FAX. 044 355 51 42

MEERESHÖHE: 531.00 m.ü.M. = +/-0.00

ÄNDERUNGEN:	ÄNDERUNGEN:	INDEX:
NULLKOTE: 0.00 = 531.00 m.ü.M.	20.02.2006 kp	A
Abluftaustritte Südfassade	28.02.2006 kp	B
Abluftaustritte Südfassade mittig Pfeileröffnung	31.03.2006 kp	C
Dachwasserrohre und Speier entfallen	18.04.2006 kp	D
Binder 1/2 IPE 500: Giebelstützenkopf; Sichtmauerwerk	26.04.2006 kp	E
Element-Mauerwerk	02.05.2006 kp	F
Element-Mauerwerk: neue Steineinteilung	12.05.2006 kp	G

BEMERKUNGEN:

SÄMTLICHE MASSE DIESES PLANES SIND ROHMASSE UND SIND VOM UNTERNEHMER ZU PRÜFEN. DIE GENAUEN MASSE FÜR DIE LIEFERUNG SIND VOM UNTERNEHMER AUF EIGENE VERANTWORTUNG AM BAU ZU KONTROLLIEREN. TYPENBEZEICHNUNGEN UND MATERIALANGABEN SIND VOM UNTERNEHMER AUF EIGENE VERANTWORTUNG ZU KONTROLLIEREN UND DURCH DEN HERSTELLER LIEFERANTEN BESTÄTIGEN ZU LASSEN.

HÖHENANGABEN BEZIEHEN SICH AUF DIE KOTE +0.00. FENSTERHÖHEN SIND JEWEILS ALS LICHTMASS DER ROHEN FENSTERÖFFNUNG ANGEGEBEN. TÜRHÖHEN SIND JEWEILS VON OK FERTIG BODEN BIS UK ROHEM STURZ ANGEGEBEN. AUSSPARUNGEN SIND AUS DEN SPEZIALPLÄNEN FÜR ELEKTRO, SANITÄR, HEIZUNG UND LÜFTUNG ZU ENTNEHMEN. BEI MASSDIFFERENZEN UND ALLFÄLLIGEN UNKLARHEITEN IST UNVERZÜGLICH MIT DER BAULEITUNG KONTAKT AUFZUNEHMEN.

LEGENDE:

- BETON
- UNTERLAGSBODEN / MÖRTEL
- BACKSTEIN
- KALKSANDSTEIN
- KUNSTSTEIN, TERRAZZO, VORFABR. BETONTEILE
- HOLZ-, SPANPLATTEN, MDF-PLATTEN
- NATURSTEIN
- GIPS, GIPSKARTON

NORDPFEIL:

N

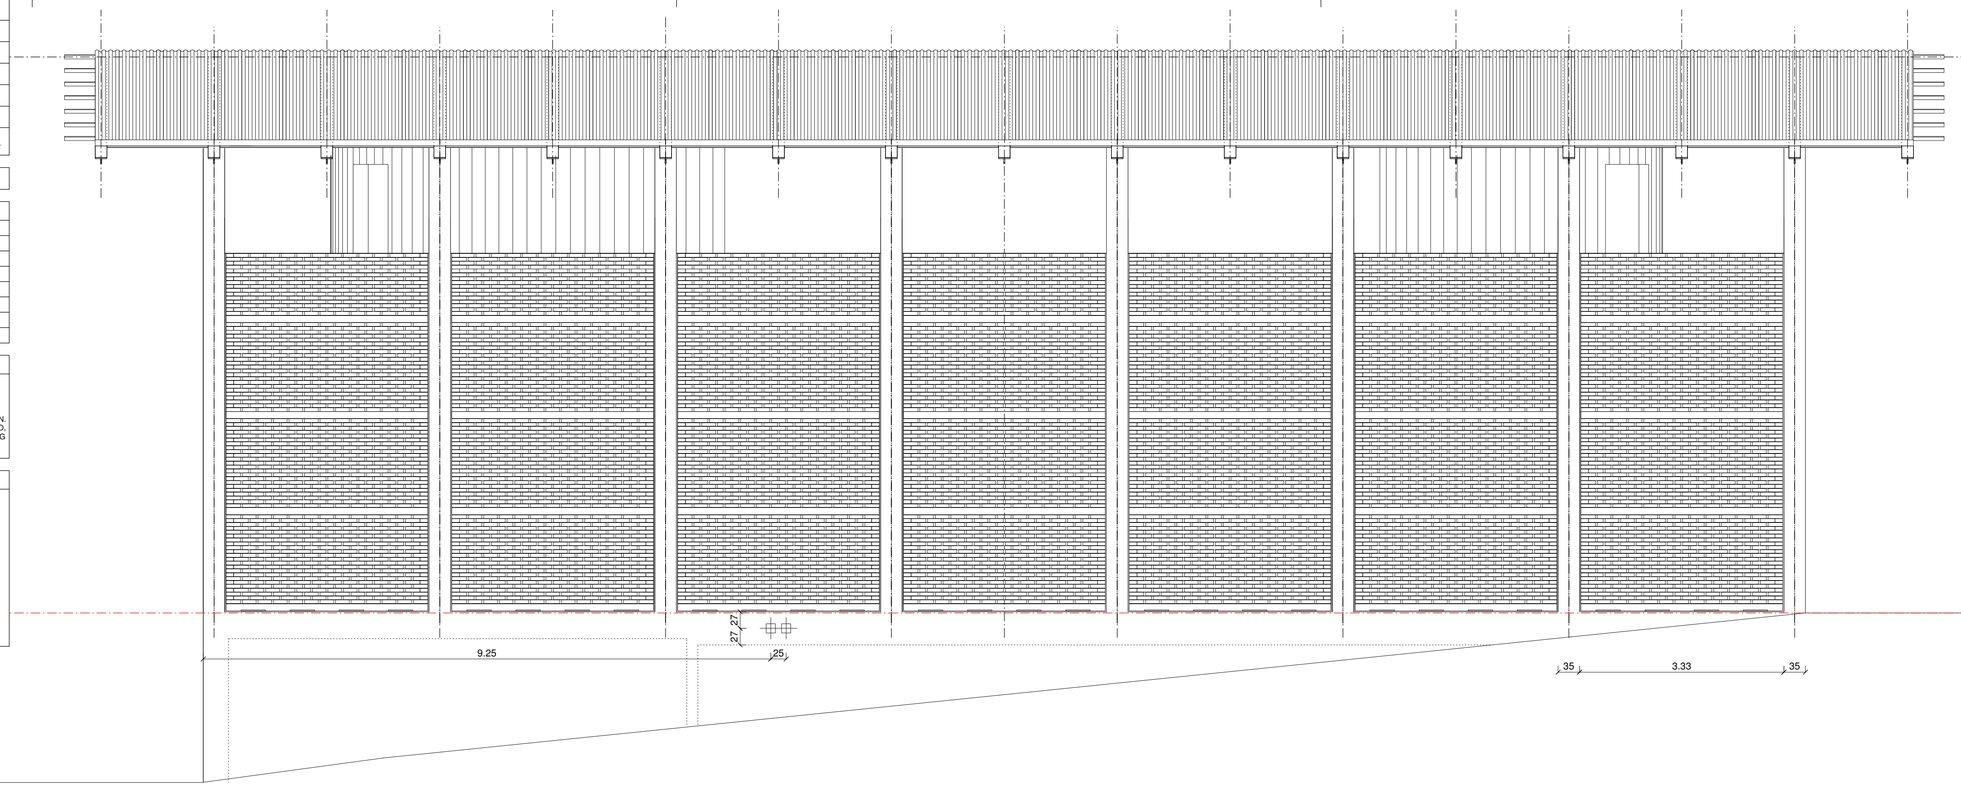

ANSICHT SÜD

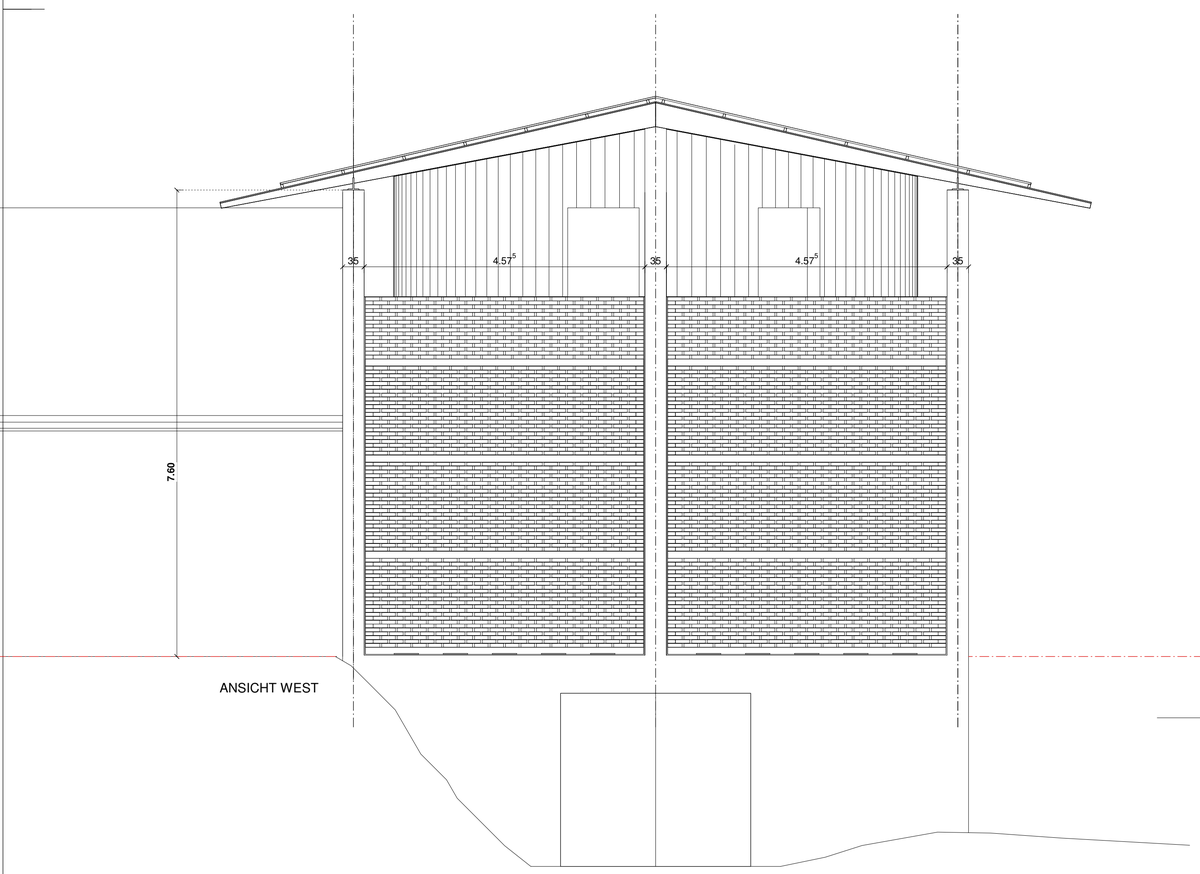

ANSICHT WEST

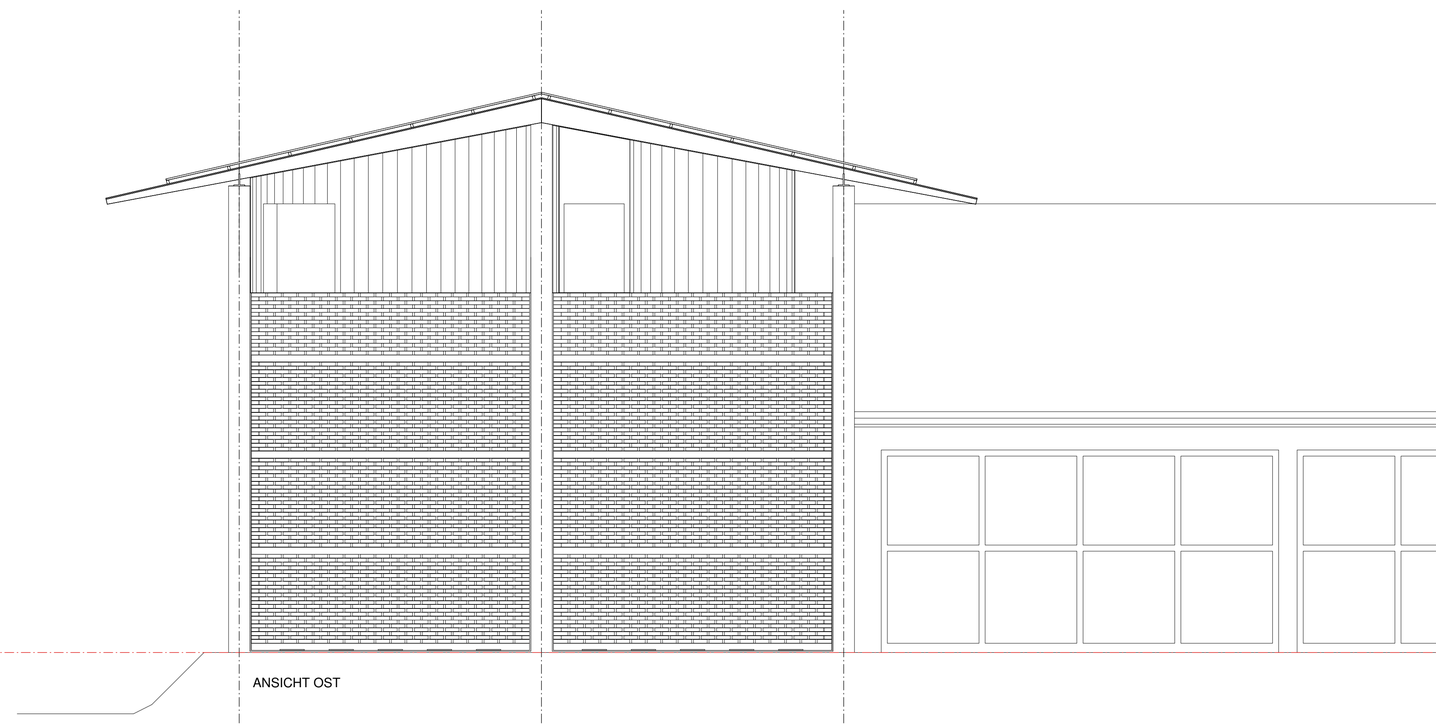

ANSICHT OST